



INGENIERIA - ARQUITECTURA

San Lucas km 45, Loja, Ecuador
cigualan@gmail.com
Telf: 0989872247

Ubicación:



Especificaciones Técnicas

Paredes	Mampostería de Ladrillo
Cubierta	Teja
Enlucidos	Cemento
Revestimientos	Empaste
Contrapisos (int.)	Ho Simple
Pisos-Baños	Cerámicos Nacional
Pisos	Cerámica y Pisos Flotante
Cielos rasos	Empastado
Puertas (int.)	MDF
Ventanas	Aluminio
Mesones	Loseta Ho Ao
Mesones Revestimiento	Cerámico
WC, Tanque Bajo	Blancos Nacional
Lavados	Blancos Nacional
Pintura Paredes	Latex

Cuadro de Áreas

Planta Baja:	81,71 m2
Planta Alta:	74,84 m2
Área Total de Construcción:	295,74 m2
Área Total de Terreno:	s/d

Sellos Municipales:

Proyecto:

DISEÑO ARQUITECTÓNICO PARA
UNA VIVIENDA UNIFAMILIAR

Proyectista:

Arq. Cesar Gualan G.
Reg. Senecyt: 1019-2019-2111581
Reg. Mun: 2303

Propietario:

Pedro Humberto
Guailas Guailas

Dibujo:

WASI & ARQ

Contiene:

- Planta Baja
- Planta Alta
- Planta de Cimentación
- Planta de Cubiertas
- Perspectivas

Clave Catastral:

S/D

Fecha:


JULIO - 2025

Escala:


Indicadas

Lámina:


1 de 3

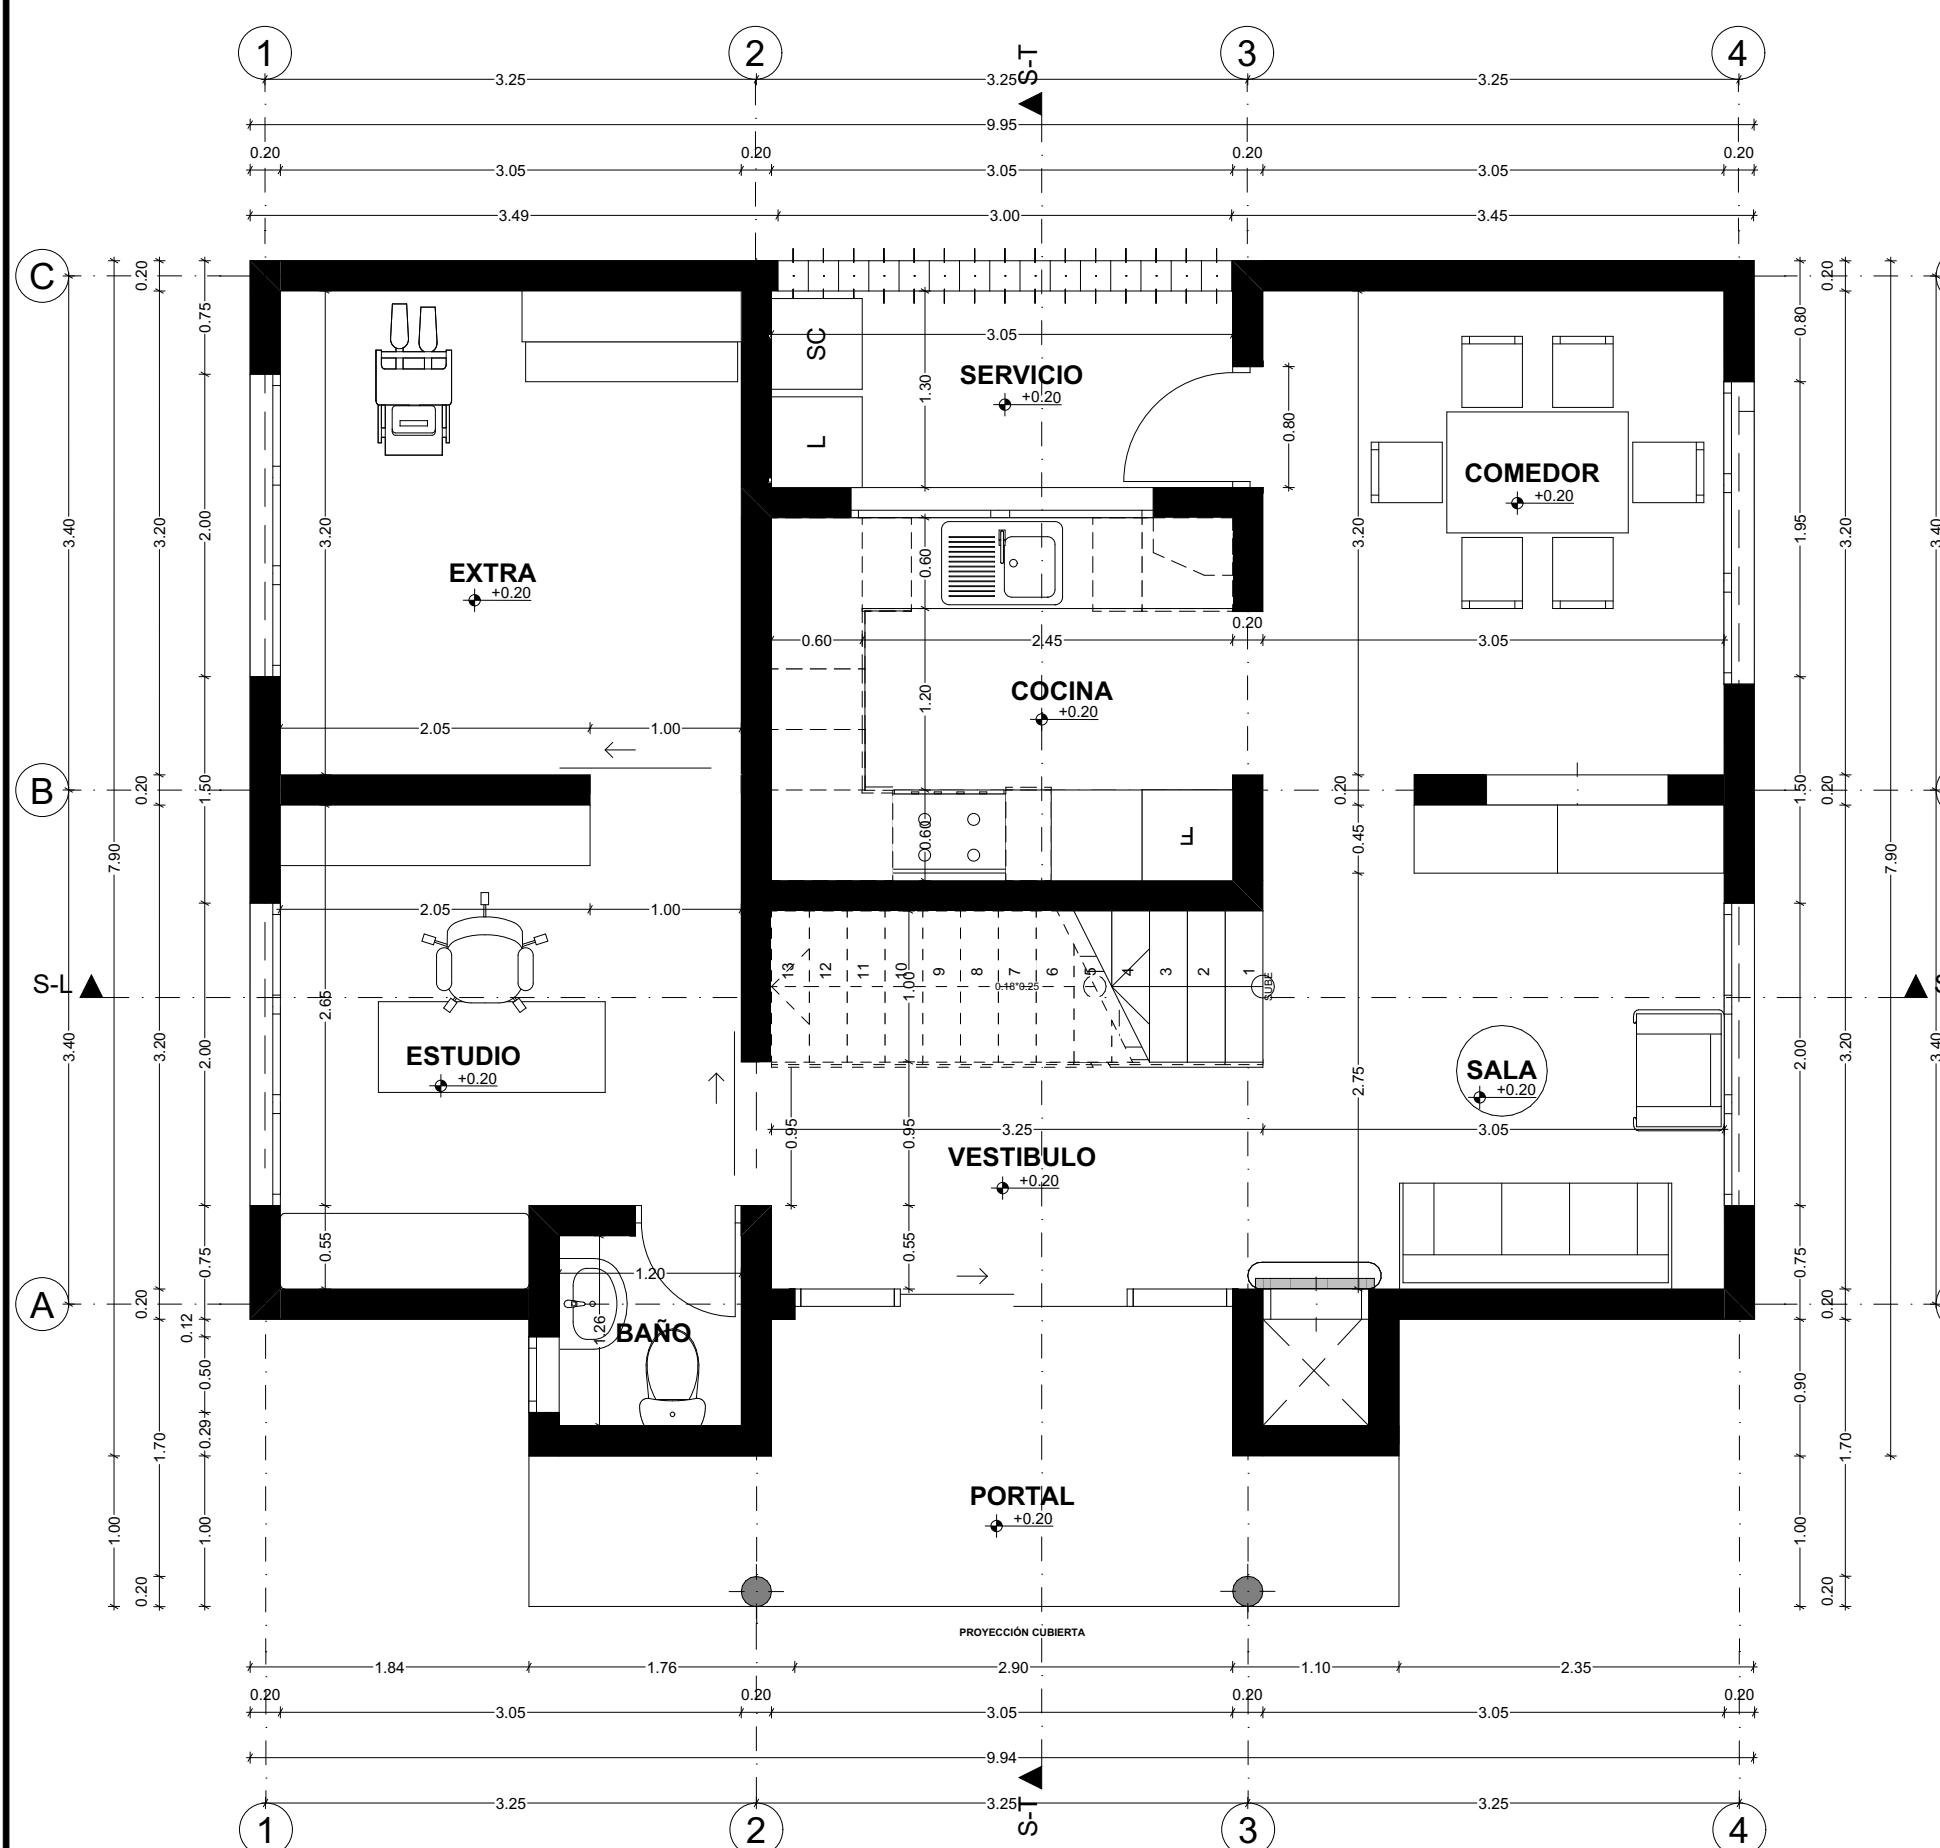


PLANTA BAJA | Esc__1:50

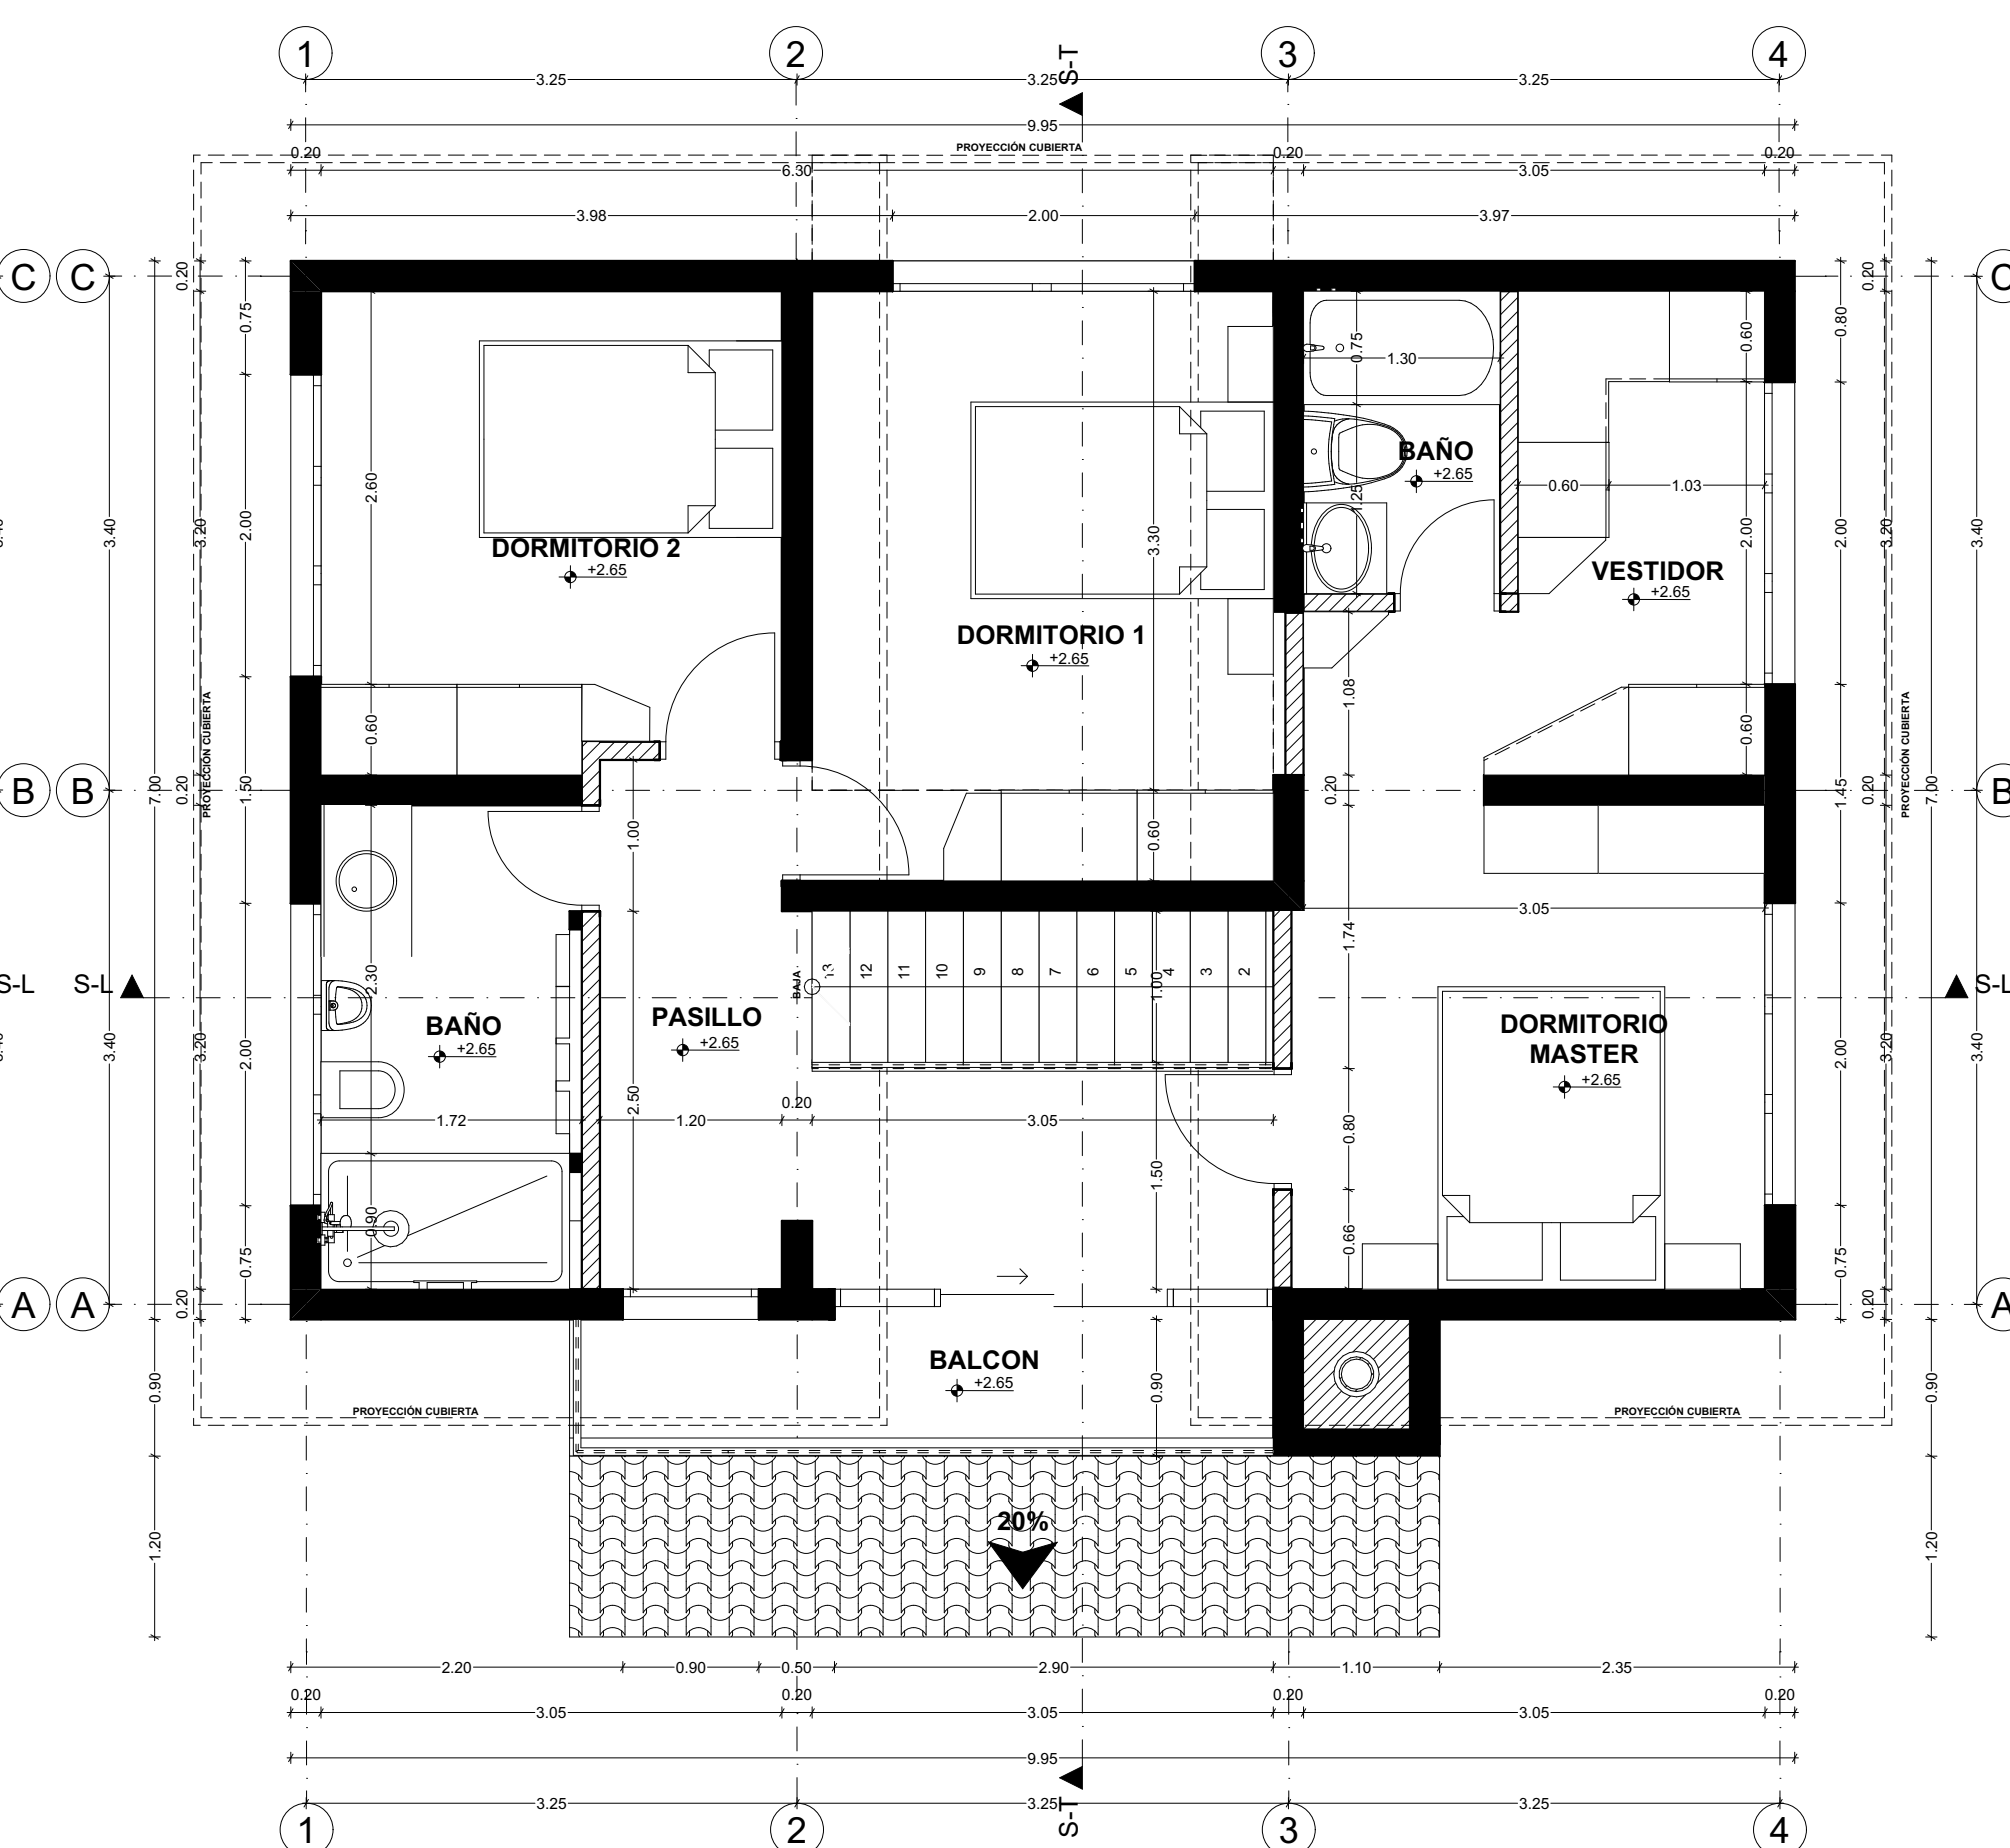

PLANTA ALTA | Esc__1:50

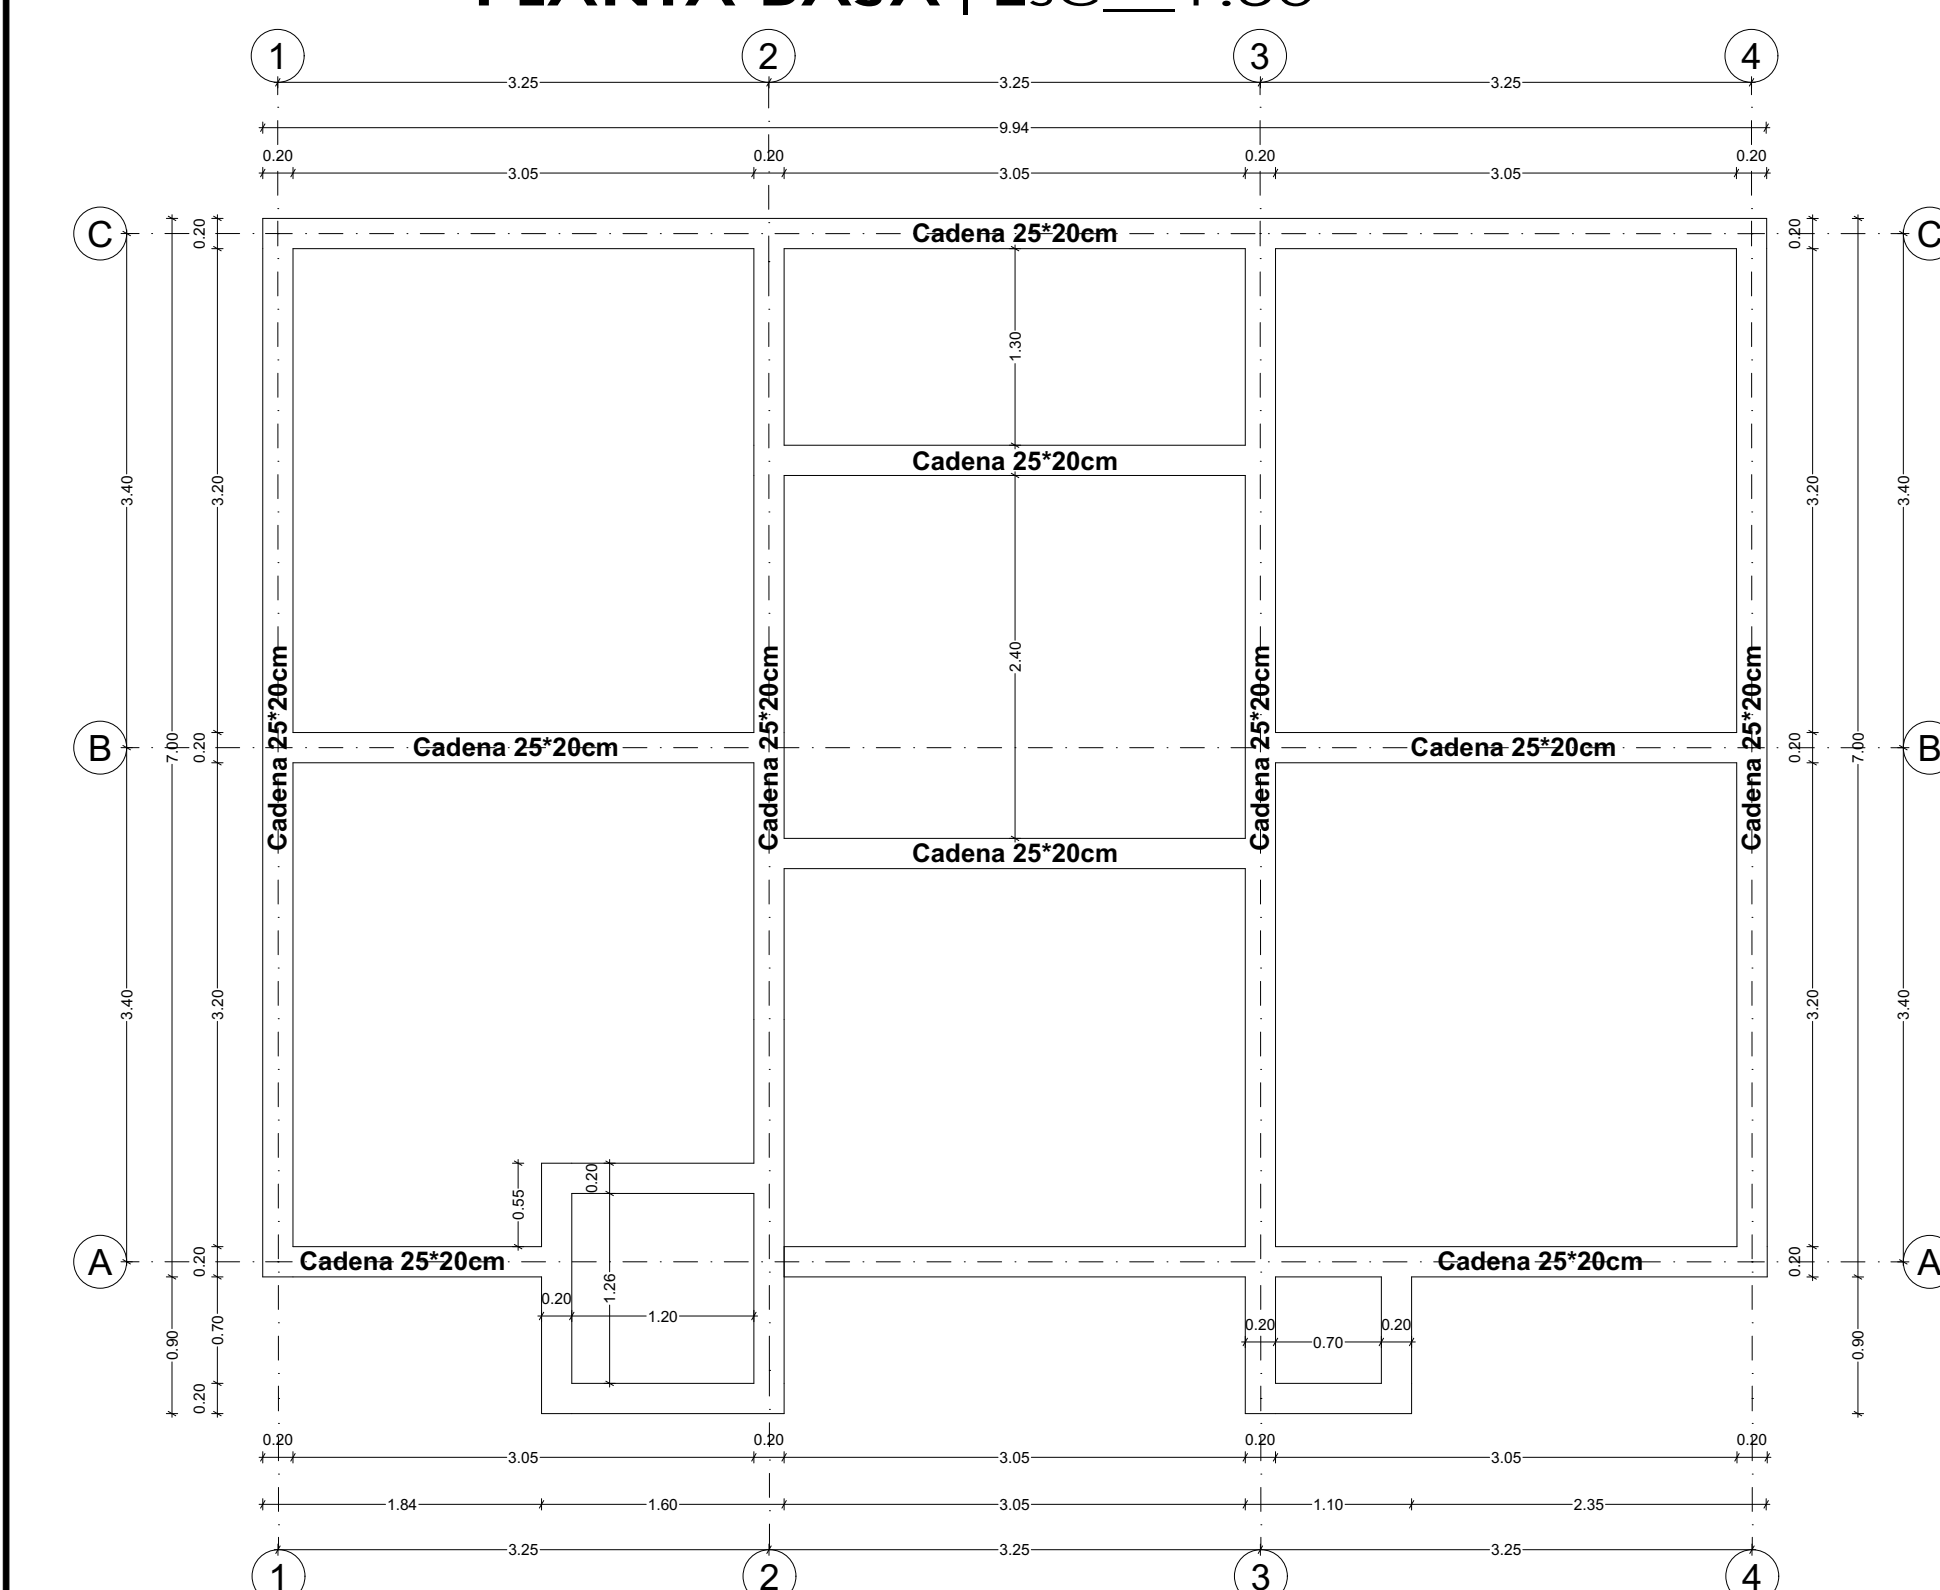

PLANTA DE CIMENTACIÓN | Esc__1:50

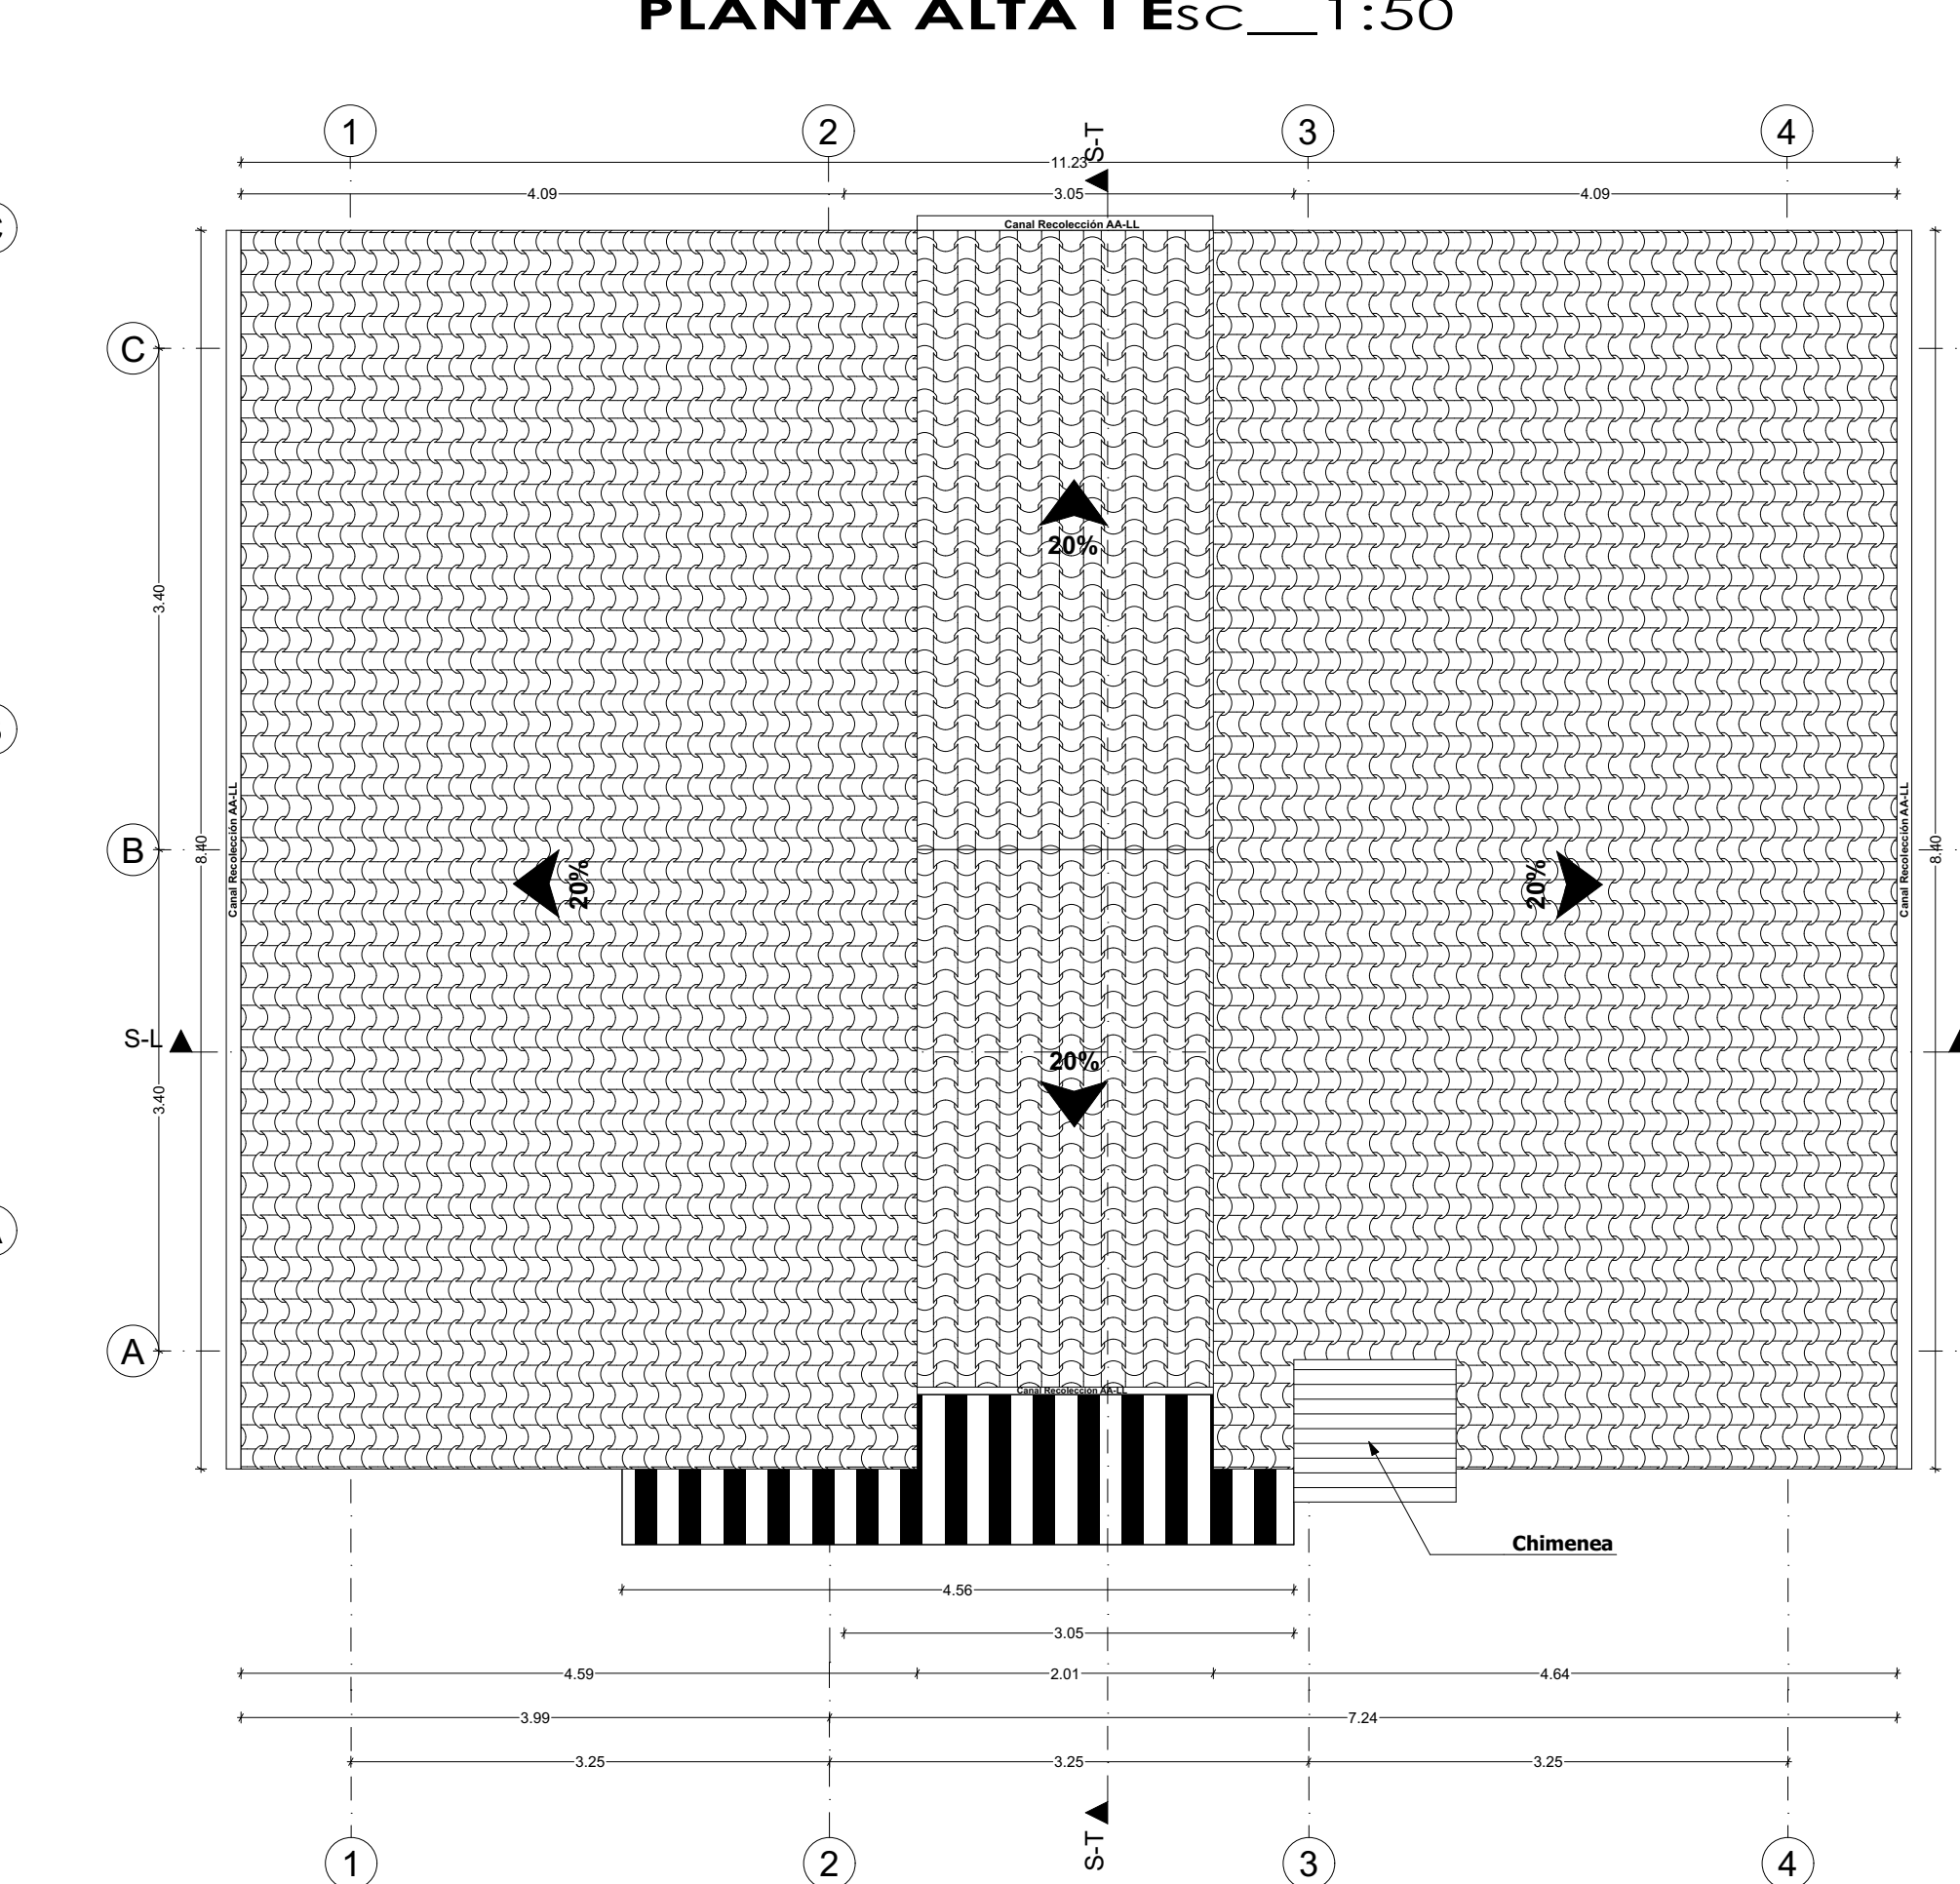

PLANTA DE CUBIERTAS | Esc__1:50



PERSPECTIVAS Planta Baja



PERSPECTIVAS Planta Alta

