



INGENIERIA - ARQUITECTURA
San Lucas km 45, Loja, Ecuador
cigualan@gmail.com
Telf: 0989872247

Ubicación :



Especificaciones Técnicas

Paredes	Mamposteria de Ladrillo
Cubierta	Teja
Enlucidos	Cemento
Revestimientos	Empaste
Contrapisos (int.)	Ho Simple
Pisos-Baños	Cerámicos Nacional
Pisos	Cerámica y Pisos Flotante
Cielosrasos	Empastado
Puertas (int.)	MDF
Ventanos	Aluminio
Mesones	Loseta Ho Ao
Mesones Revestimiento	Cerámico
WC, Tanque Bajo	Blancos Nacional
Lavados	Blancos Nacional
Pintura Paredes	Latex

Cuadro de Áreas

Planta Baja:	81.71 m2
Planta Alta:	74.84 m2
Área Total de Construcción:	295.74 m2
Área Total de Terreno:	s/d

Sellos Municipales:

Proyecto:

DISEÑO ARQUITECTÓNICO PARA
UNA VIVIENDA UNIFAMILIAR

Proyectista:

Arq. Cesar Gualan G.
Reg. Senescyt: 1019-2019-2111581
Reg. Mun: 2303

Propietario:

Pedro Humberto
Guailas Guailas

Dibujo:

WASI & ARQ

Contiene:

- Instalaciones Eléctricas
- Instalaciones Hidrosanitarias

Clave
Catastral:

S/D

Fecha:


JULIO - 2025

Escala:


Indicadas

Lámina:


3 de 3

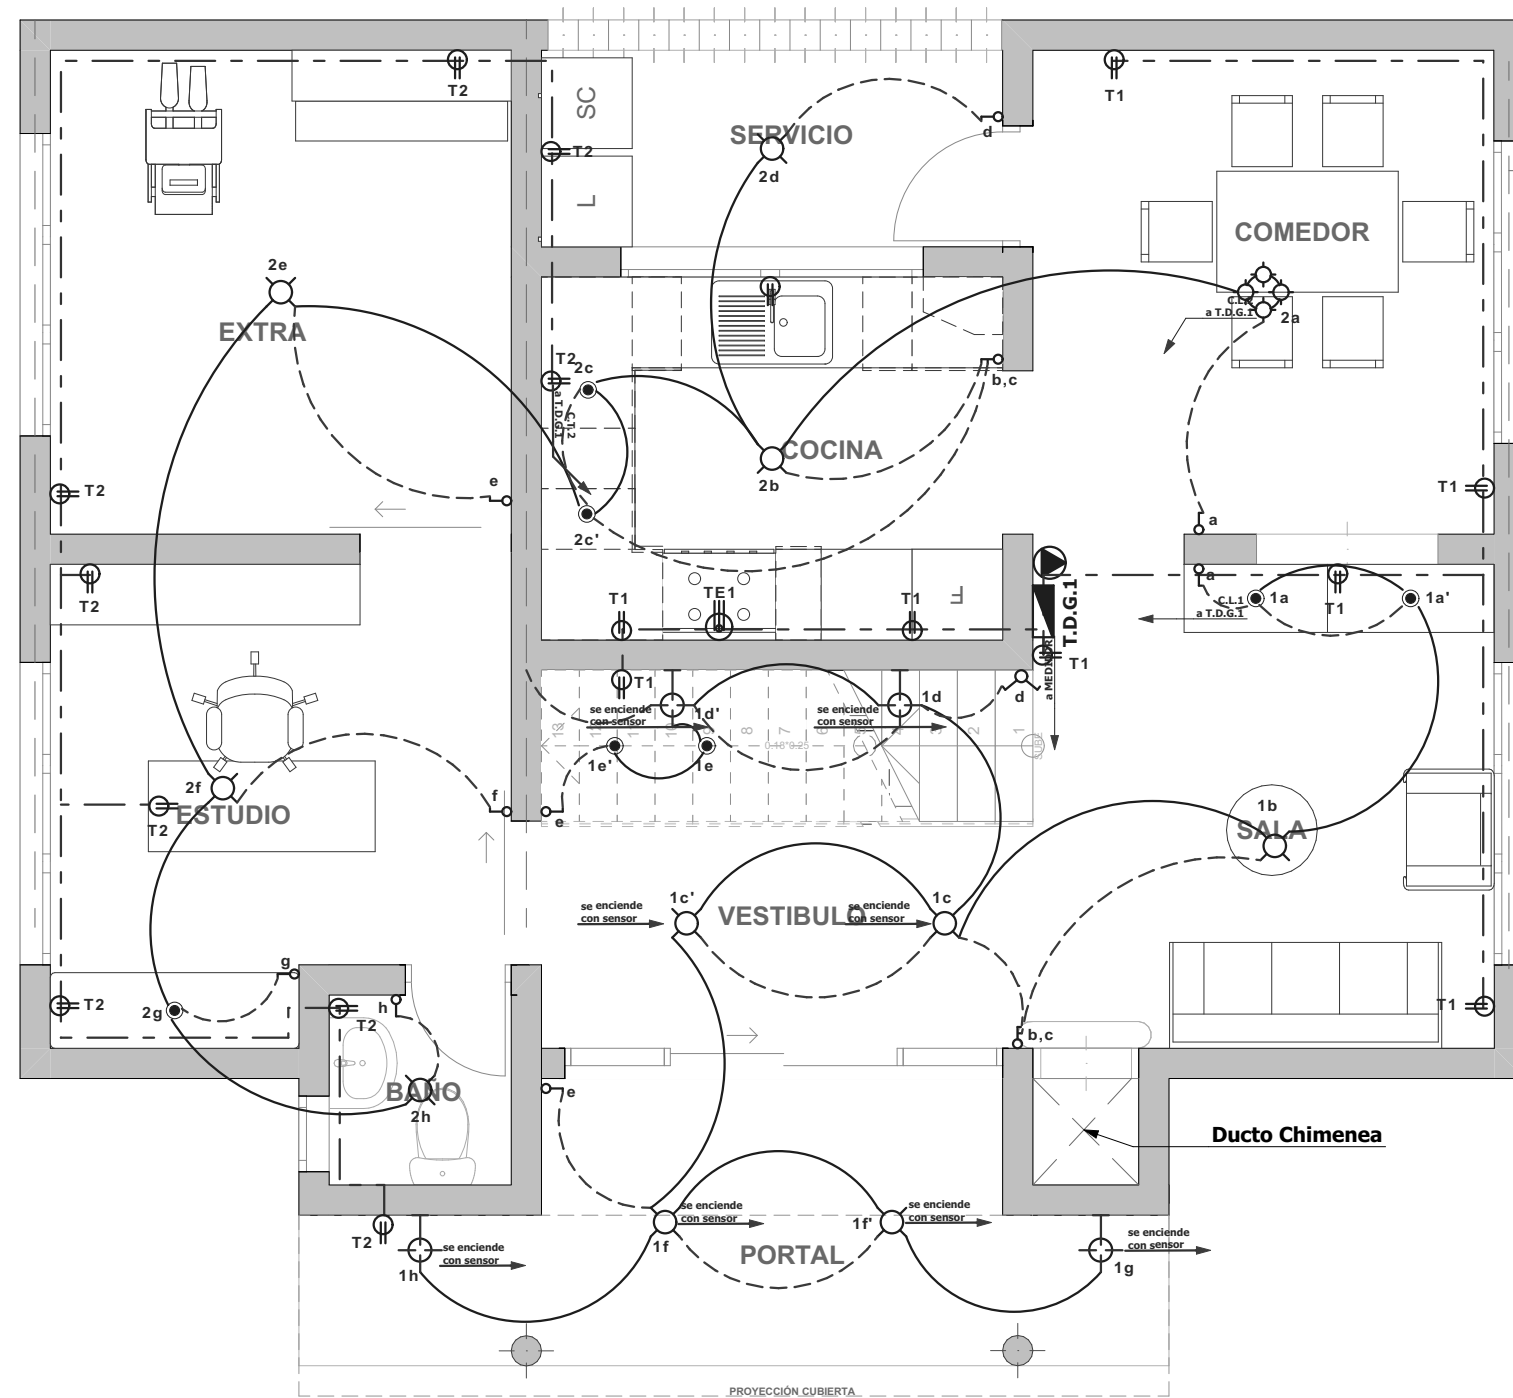


PLANTA BAJA | Esc 1:50

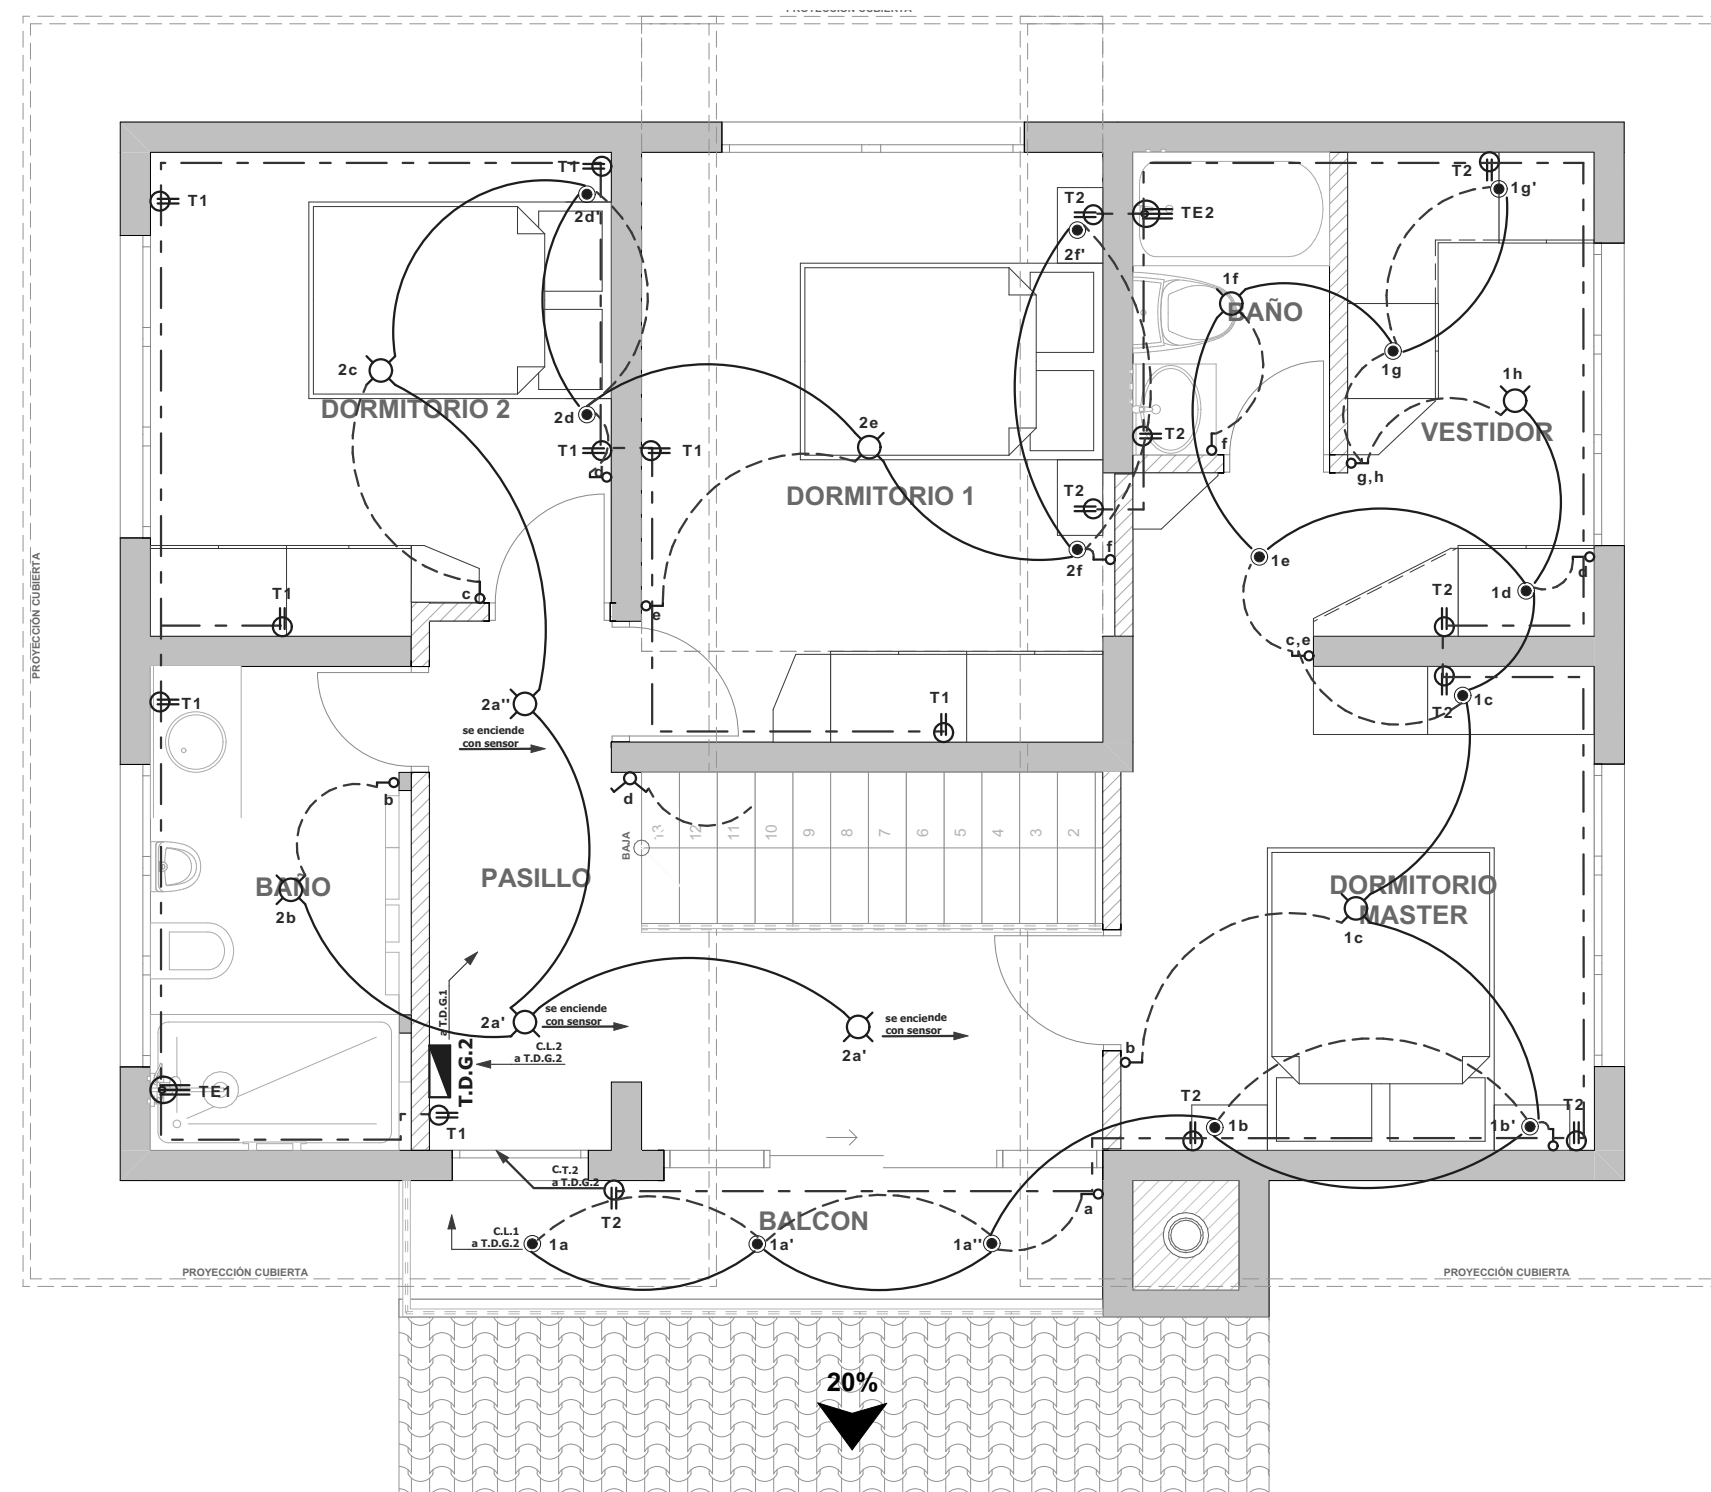

PLANTA ALTA I | Esc 1:50

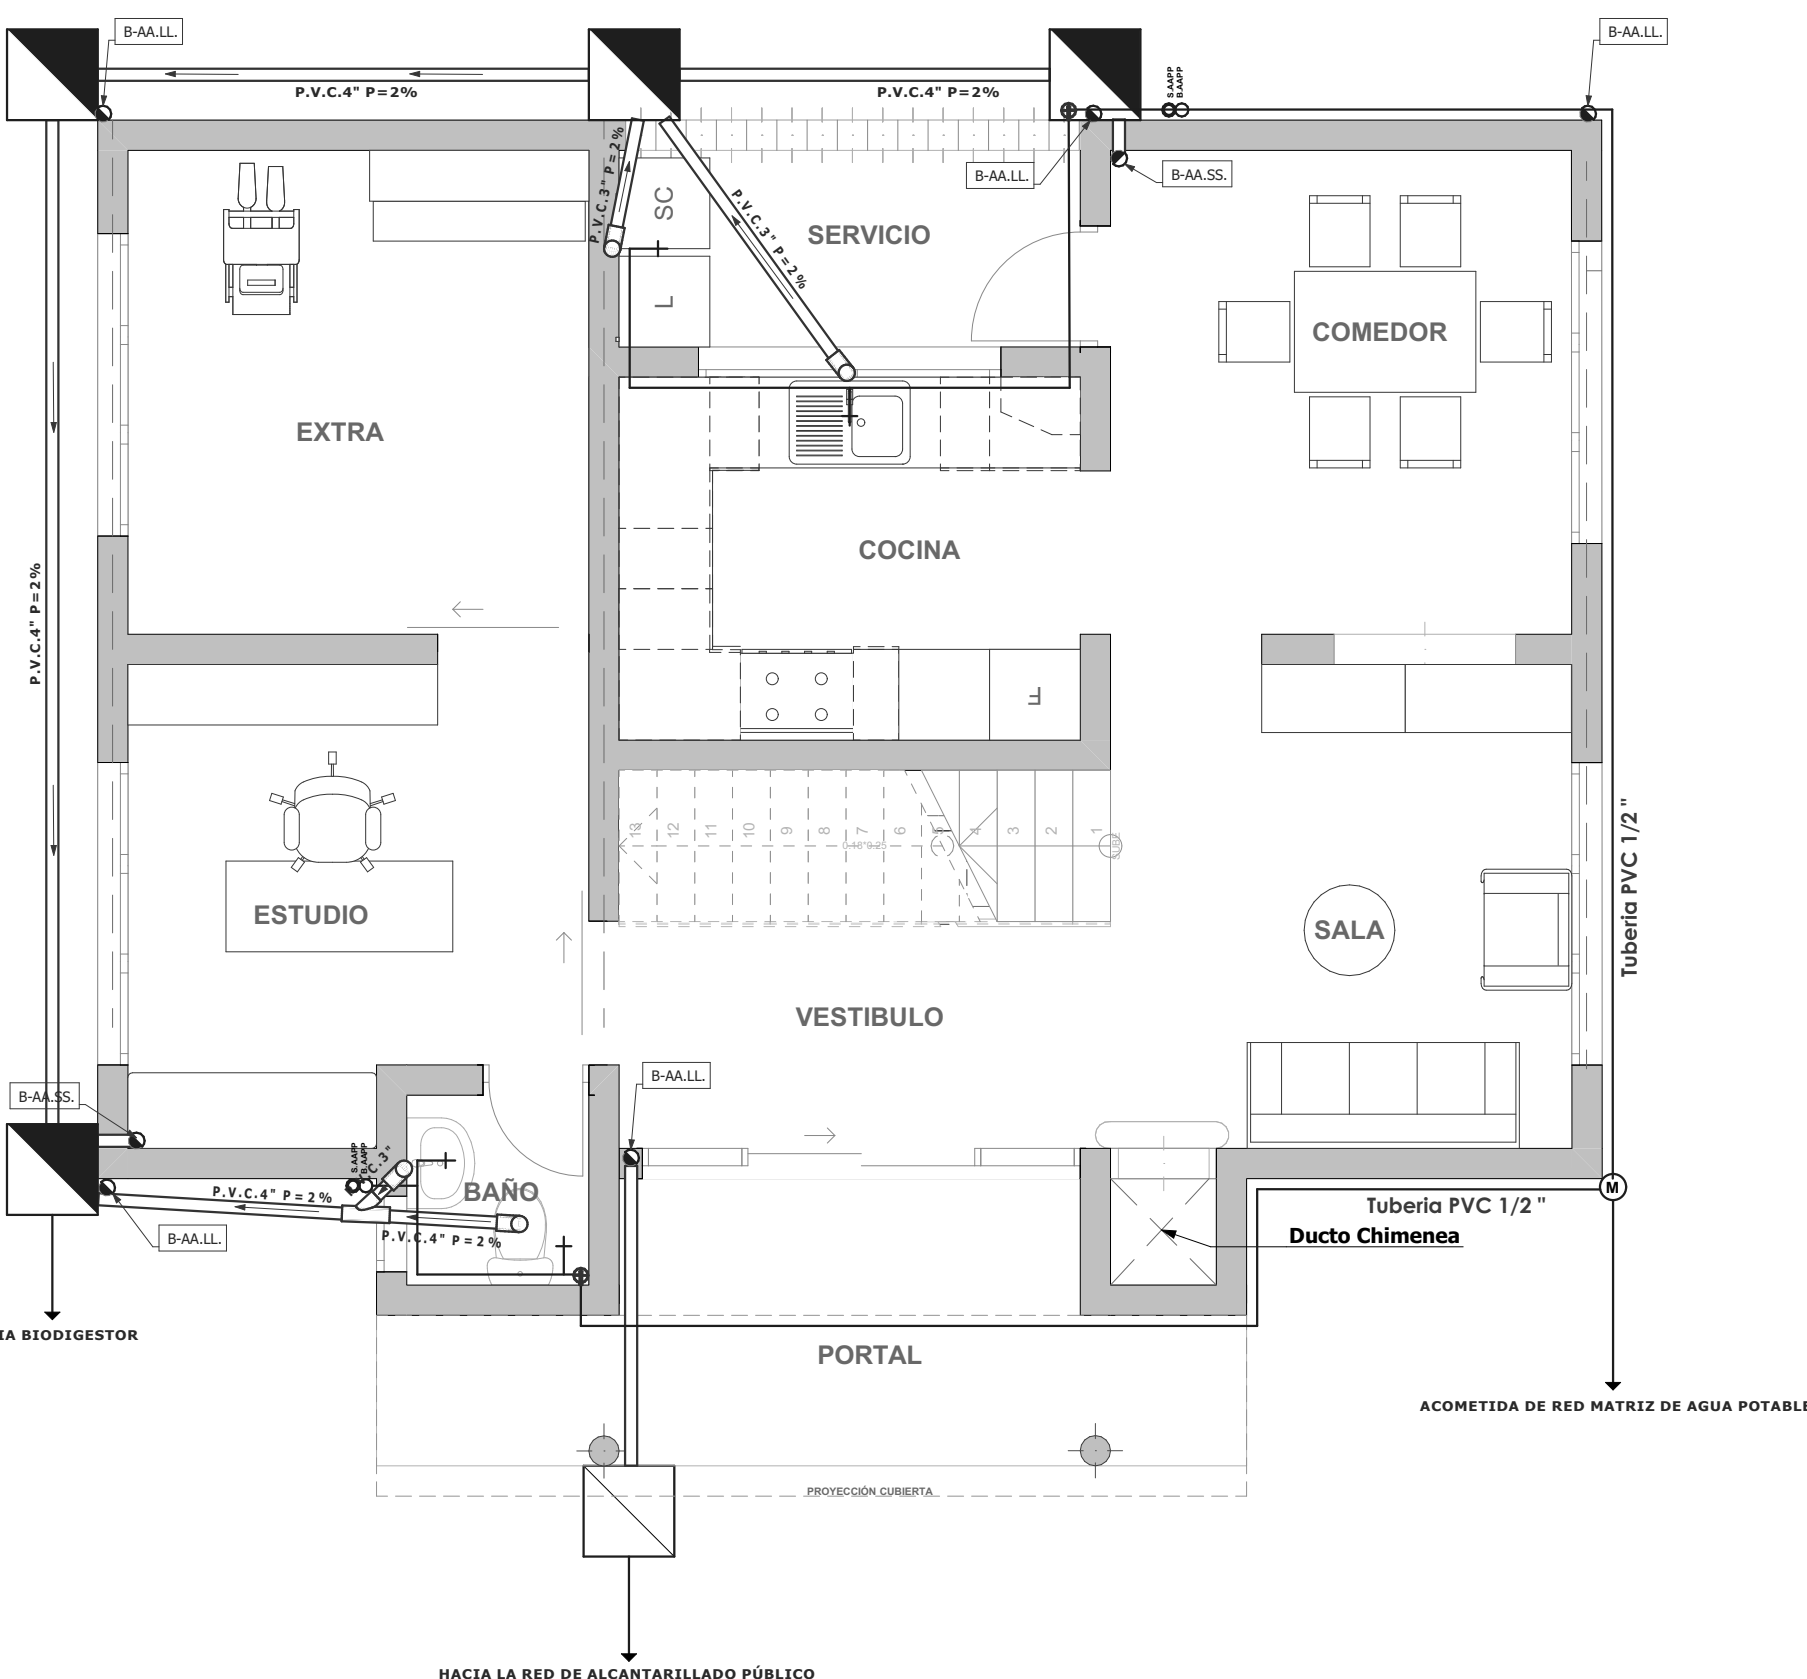

PLANTA BAJA | Esc 1:50

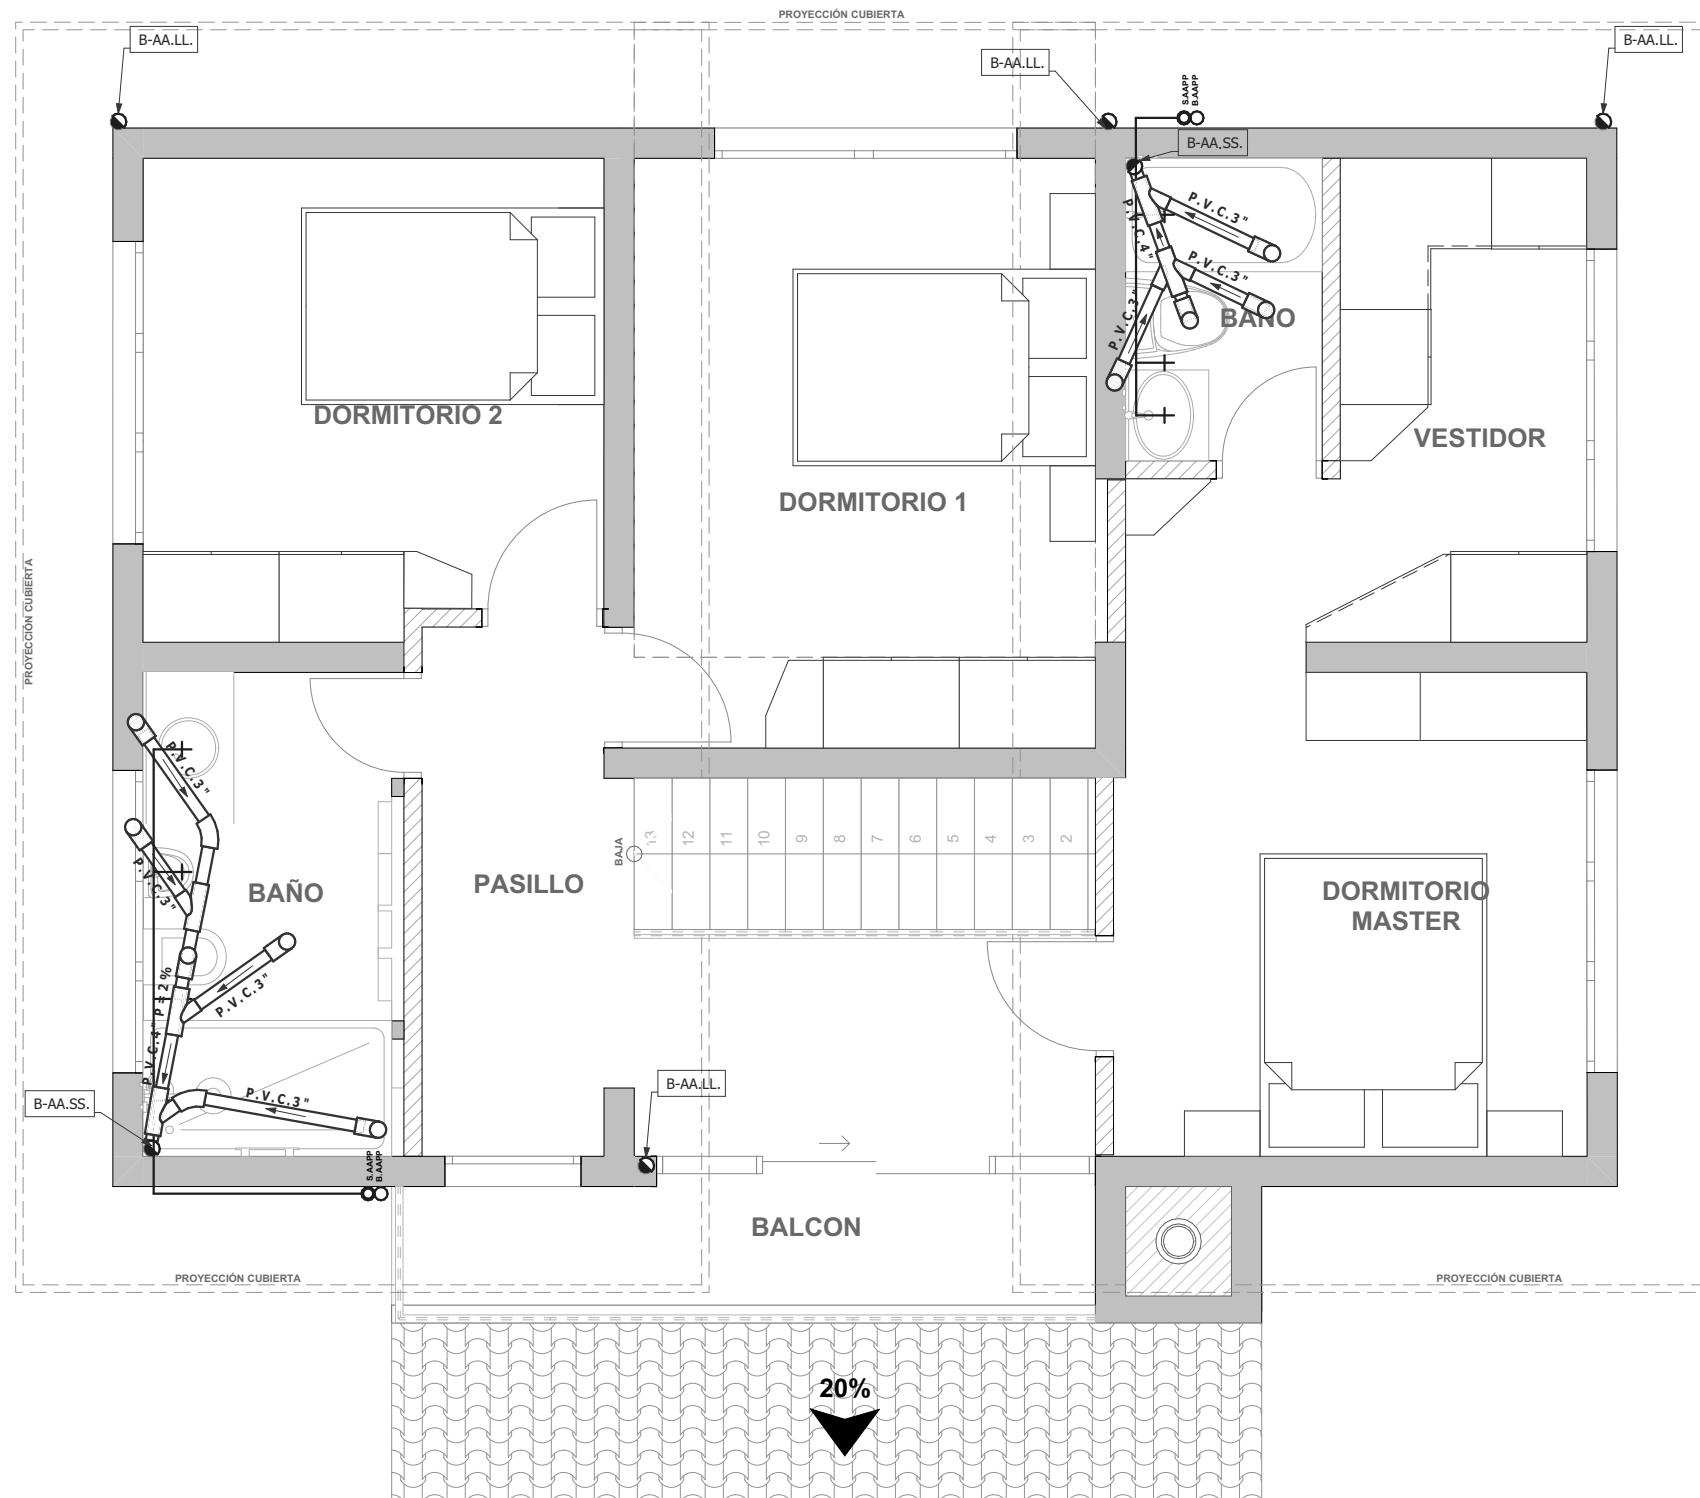

PLANTA ALTA I | Esc 1:50

INSTALACIONES ELECTRICAS			
SIMBOLOGIA			
	LUMINARIA INCANDESCENTE		PORTERO ELÉCTRICO
	LAMPARA DECORATIVA		TELEFONO
	REFLECTOR DE JARDÍN		MEDIDOR DE LUZ
	TOMACORRIENTE POLARIZADO		TABLERO DE DISTRIBUCION GENERAL
	TOMACORRIENTES ESPECIALES 220V		TABLERO DE DISTRIBUC. SECUNDARIO
	INTERRUPTOR SIMPLE, DOBLE, TRIPLE		RED DE TOMACORRIENTES
	CONMUTADOR SIMPLE, DOBLE		RED LUMINARIAS
	CONMUTADOR SIMPLE		RED INTERRUPTORES
	OJO DE BUEY		SALIDA ESPECIAL
	APLIQUE DE PARED		TV CABLE

INSTALACIONES SANITARIAS			
SIMBOLOGIA			
	medidor de agua		bajante de AA.SS
	llave cortadora		punto de desagüe de AA.SS
	columna de AA.PP		bajante de AA.LL
	red de AA.PP		red de AA.SS
	sumidero de AA.LL		red de AA.LL
	sumidero de piso		caja de revisión de AA.LL
	caja de revisión de AA.SS.		calefón